
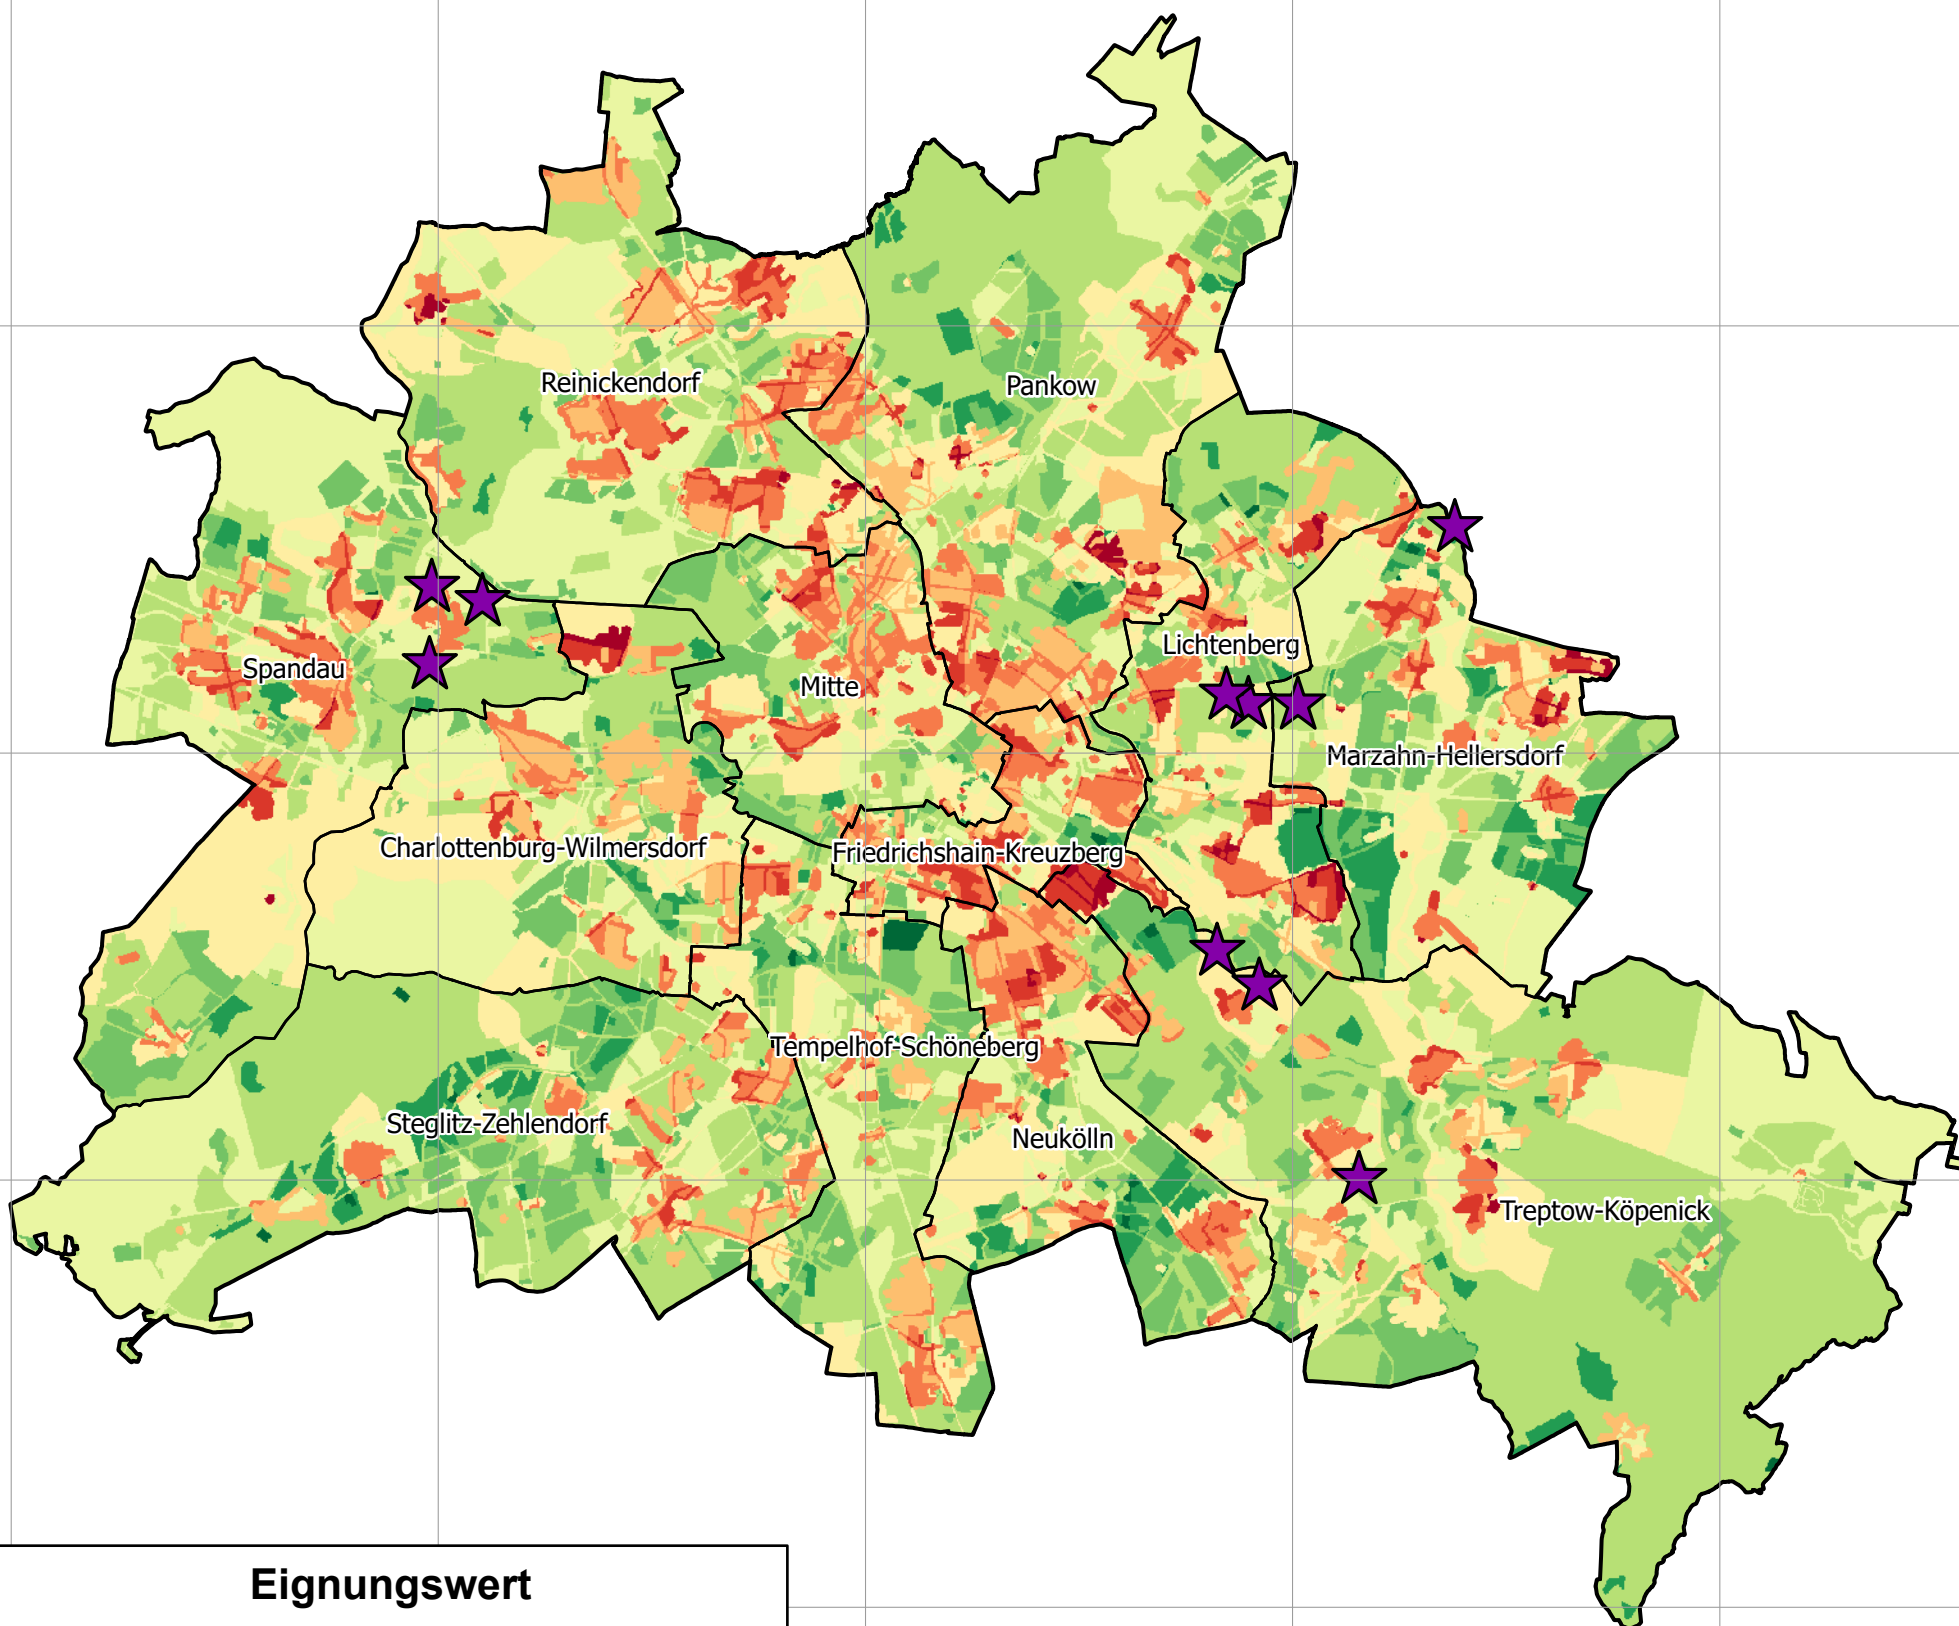


Wo sollten neue Grundschulen in Berlin gebaut werden?

Standortanalyse für neue Grundschulen in Berlin

Eignungsbewertung auf Basis von Bedarf, Erreichbarkeit und Flächennutzung

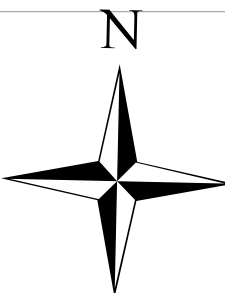

Eignungswert




★ Die 10 besten Kandidaten

Maßstab 1:272.000

Erreichbarkeit bestehender Grundschulen

Analyse mittels Network Analyst innerhalb eines 1-km-Fußwegradius

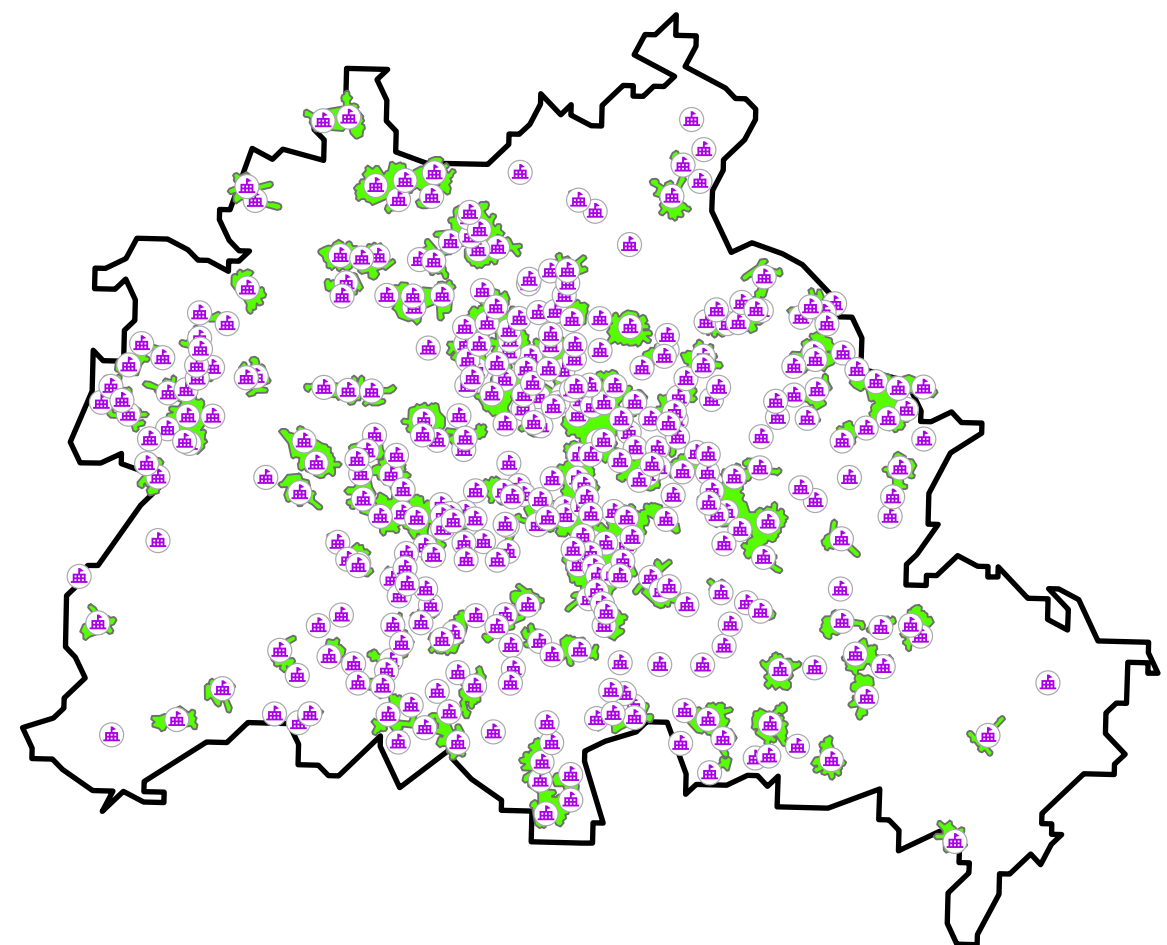


Legende

- verfügbare Grundschule
- Erreichbarkeitszone (1 km)
- Berliner Grenze

Maßstab 1:500.000

Bedarfsdeckung nach Einschulbereich

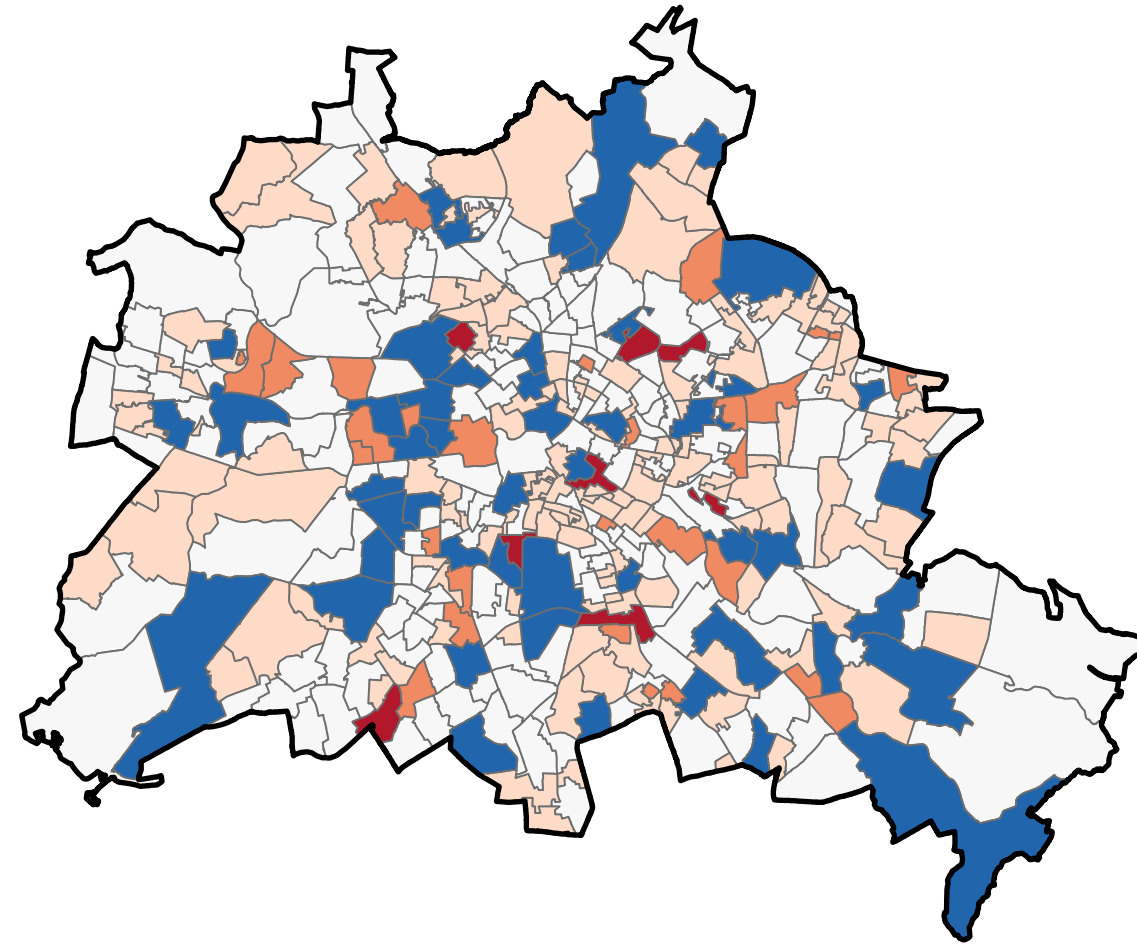

Bedarfs-Kapazitäts-Differenz

- Kapazitätsüberschuss
- Ausgeglichen / geringer Bedarf
- Mittlerer Bedarf
- Hoher Bedarf
- Sehr hoher Bedarf

Maßstab 1:500.000

Die 10 besten Standorte für neue Grundschulen

Rang	Kandidat	Bezirk	FNP-Nutzungsart	Koordinaten (WGS84)	Bemerkung
1	C-01	Marzahn-Hellersdorf	Gewerbliche Baufläche	52.5316, 13.5277	Rechteckige Fläche, direkter Straßenanschluss, geringster Umwidmungsaufwand
2	C-02	Lichtenberg	Gewerbliche Baufläche	52.5333, 13.5030	Beste verkehrliche Anbindung, direkt an Hauptmagistrale, Kreisverkehr angrenzend
3	C-03	Marzahn-Hellersdorf	Gemeinbedarfsfläche mit hohem Grünanteil	52.5696, 13.5807	Einzige Fläche mit Gemeinbedarfswidmung, Baumfällung u. schmale Zufahrt zu prüfen
4	C-04	Spandau	Gebäude- und Freifläche, Mischnutzung mit Wohnen	52.5495, 13.2455	ÖPNV-Haltestellen direkt angrenzend, unregelmäßige Grundstücksform
5	C-05	Spandau	Wohnbaufläche, W2 (GFZ bis 1,5)	52.5526, 13.2277	Ideale soziale Lage (REWE, Kita, ÖPNV), Wohnbaufläche — B-Plan-Prüfung erforderlich
6	C-06	Lichtenberg	Gewerbliche Baufläche	52.5315, 13.5107	Nähe zu Bestandsschule, kleinere Fläche, Anbindung an Hauptverkehr schwächer
7	C-07	Treptow-Köpenick	Gewerbliche Baufläche	52.4320, 13.5521	Wohnnähe positiv, Immissionskonflikt durch Kfz-Gewerbe (Lärm/Geruch)
8	C-08	Treptow-Köpenick	Gewerbliche Baufläche	52.4794, 13.5016	L-förmiger Zuschnitt, schmale Erschließungsstraße, gewerblich-kreatives Umfeld
9	C-09	Treptow-Köpenick	Wohnbaufläche, W4 (GFZ bis 0,4) mit landschaftlicher Prägung	52.4723, 13.5164	GFZ 0,4 — planungsrechtlich kaum bebaubar, dichter Baumbestand
10	C-10	Spandau	Gewerbliche Baufläche	52.5359, 13.2278	Spreeufer — Hochwasser-/Gewässerrandstreifenprüfung, informelle Bebauung zu räumen